


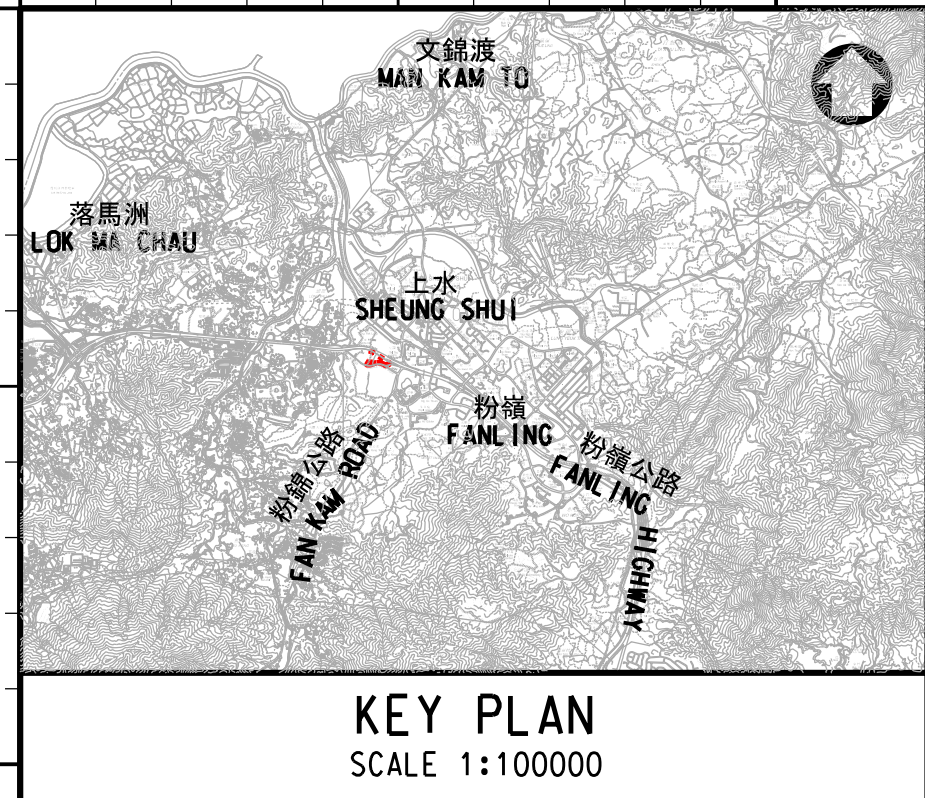

在工務計劃項目第7828CL號
古洞北新發展區及粉嶺北新發展區
餘下地盤平整和基礎設施工程中擬議道路工程
(只供示意用途)
PROPOSED ROAD WORKS UNDER PWP ITEM NO. 7828CL
REMAINING PHASE OF SITE FORMATION AND
ENGINEERING INFRASTRUCTURE WORKS AT
KWU TUNG NORTH NEW DEVELOPMENT AREA
AND FANLING NORTH NEW DEVELOPMENT AREA
(FOR INDICATION PURPOSE ONLY)

- 註釋 NOTES:
- 除特別註明外，全部以米為度量單位。
ALL DIMENSIONS ARE IN METERS UNLESS OTHERWISE STATED.
 - 所有水平均為約數以米為單位，並在香港主水平基準上。
ALL LEVELS ARE APPROXIMATE VALUES AND IN METRES ABOVE HONG KONG PRINCIPAL DATUM.
 - 如有需要，施工區界線內部分現有的停車灣、行車道、行人路及安全島或分階段暫時封閉。
SECTIONS OF THE EXISTING LAY-BY CARRIAGEWAYS, FOOTPATHS AND TRAFFIC ISLANDS WITHIN THE LIMIT OF WORKS AREA MAY BE TEMPORARILY CLOSED IN PHASES AS AND WHEN REQUIRED.

- 圖例 LEGEND:
- 擬議工地平整、排污、排水、供水、道路及路口改善工程施工區介限 (註釋3)
 - 擬議發展地盤 PROPOSED DEVELOPMENT SITE
 - 擬議污水渠 PROPOSED SEWERS
 - 擬議供水管 PROPOSED WATER SUPPLY PIPE
 - 擬議雨水渠 PROPOSED STORMWATER DRAIN
 - 原有明渠將改建為箱形暗渠 EXISTING NULLAH TO BE CONVERTED INTO BOX CULVERT
 - 擬建排水出口 PROPOSED OUTLET
 - 擬建隔音罩 PROPOSED NOISE ENCLOSURE
 - 擬建懸臂式隔音屏障 PROPOSED CANTILEVER NOISE BARRIER
 - 擬議工地平整工程 PROPOSED SITE FORMATION WORKS
 - 擬議道路工程 PROPOSED ROAD WORKS
 - 擬議行人道工程 PROPOSED PEDESTRIAN WALKWAY WORKS
 - 擬議行人過路處 PROPOSED PEDESTRIAN CROSSING
 - 擬議巴士停車灣 PROPOSED BUS STOP LAY-BY
 - 擬議的士站 PROPOSED TAXI STAND
 - 擬議車輛進出入口 PROPOSED VEHICLE INGRESS / EGRESS
 - 擬議緊急車輛通道 PROPOSED EMERGENCY VEHICULAR ACCESS

詳情見附錄一
REFER TO ANNEX 1

工程名稱 PROJECT TITLE
工務計劃項目第B869CL號
上水大頭嶺公共房屋發展
之工地平整及基礎設施工程
PWP ITEM NO. B869CL
SITE FORMATION AND INFRASTRUCTURE
WORKS FOR PUBLIC HOUSING DEVELOPMENTS
AT TAI TAU LENG

圖則名稱 PLAN TITLE
擬議工地平整及基礎設施工程平面圖
(五張之第一張)
LAYOUT PLAN FOR SITE FORMATION
AND INFRASTRUCTURE WORKS
(SHEET 1 OF 5)

圖則編號 PLAN NO.
附錄二
ANNEX 2

部門 OFFICE
北拓展處
NORTH DEVELOPMENT OFFICE

土木工程拓展署
Civil Engineering and
Development Department

連接線
CUT LINE
圖則 ANNEX 2
(五張之第二張)
PLAN NO. ANNEX 2
(SHEET 2 OF 5)



KEY PLAN
SCALE 1:100000

連接線
CUT LINE
圖則 ANNEX 2
(五張之第一張)
PLAN NO. ANNEX 2
(SHEET 1 OF 5)

註釋 NOTES:

- 除特別註明外，全部以米為量度單位。
ALL DIMENSIONS ARE IN METERS UNLESS OTHERWISE STATED.
- 所有水平均為約數以米為單位，並在香港主水平基準上。
ALL LEVELS ARE APPROXIMATE VALUES AND IN METRES ABOVE HONG KONG PRINCIPAL DATUM.
- 如有需要，施工區界線內部分現有的停車灣、行車道、行人路及安全島或分路段暫時封閉。
SECTIONS OF THE EXISTING LAY-BY, CARRIAGeways, FOOTPATHS AND TRAFFIC ISLANDS WITHIN THE LIMIT OF WORKS AREA MAY BE TEMPORARILY CLOSED IN PHASES AS AND WHEN REQUIRED.

圖例 LEGEND:

- 擬議工地平整、排污、排水、供水、道路及路口改善工程施工區介限 (註釋3)
LIMIT OF WORKS AREA FOR PROPOSED SITE FORMATION, SEWERAGE, DRAINAGE, WATER SUPPLY, ROAD AND JUNCTION IMPROVEMENT WORKS (NOTE 3)
- 擬議發展地盤
PROPOSED DEVELOPMENT SITE
- 擬議污水渠
PROPOSED SEWERS
- 擬議供水管
PROPOSED WATER SUPPLY PIPE
- 擬議雨水渠
PROPOSED STORMWATER DRAIN
- 原有明渠將改建為箱形暗渠
EXISTING NULLAH TO BE CONVERTED INTO BOX CULVERT
- 擬建排水出口
PROPOSED OUTLET
- 擬建隔音罩
PROPOSED NOISE ENCLOSURE
- 擬建懸臂式隔音屏障
PROPOSED CANTILEVER NOISE BARRIER
- 擬議工地平整工程
PROPOSED SITE FORMATION WORKS
- 擬議道路工程
PROPOSED ROAD WORKS
- 擬議行人道工程
PROPOSED PEDESTRIAN WALKWAY WORKS
- 擬議行人過路處
PROPOSED PEDESTRIAN CROSSING
- 擬議巴士停車灣
PROPOSED BUS STOP LAY-BY
- 擬議的士站
PROPOSED TAXI STAND
- 擬議車輛進出入口
PROPOSED VEHICLE INGRESS / EGRESS
- 擬議緊急車輛通道
PROPOSED EMERGENCY VEHICULAR ACCESS

工程名稱 PROJECT TITLE
工務計劃項目第B869CL號
上水大頭嶺公共房屋發展
之工地平整及基礎設施工程
PWP ITEM NO. B869CL
SITE FORMATION AND INFRASTRUCTURE
WORKS FOR PUBLIC HOUSING DEVELOPMENTS
AT TAI TAU LENG



圖則名稱 PLAN TITLE
擬議工地平整及基礎設施工程平面圖
(五張之第二張)
LAYOUT PLAN FOR SITE FORMATION
AND INFRASTRUCTURE WORKS
(SHEET 2 OF 5)

圖則編號 PLAN NO.
附錄二
ANNEX 2

比例 SCALE
1:1000

部門 OFFICE
北拓展處
NORTH DEVELOPMENT OFFICE

CEDD 土木工程拓展署
Civil Engineering and
Development Department

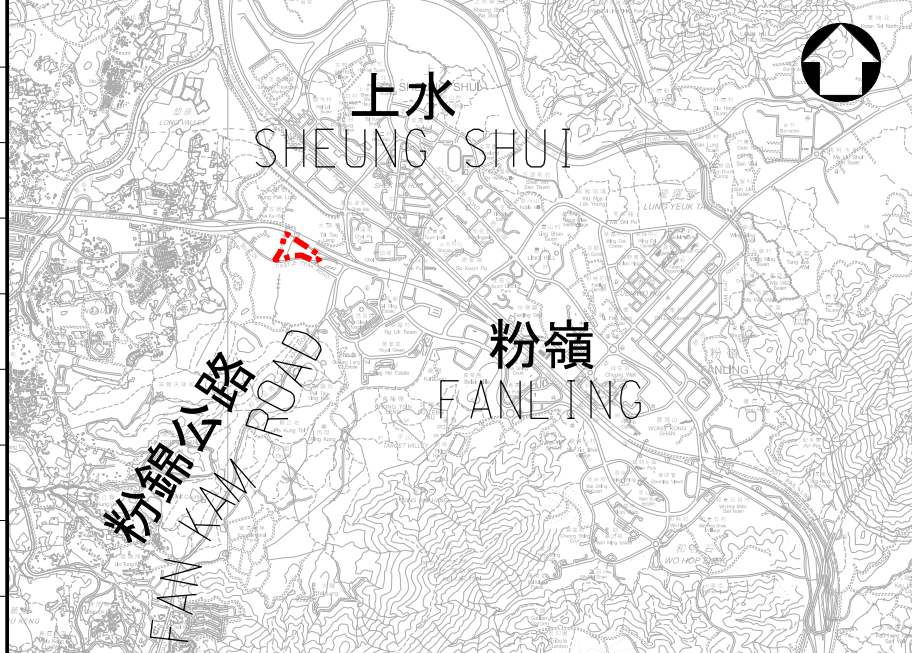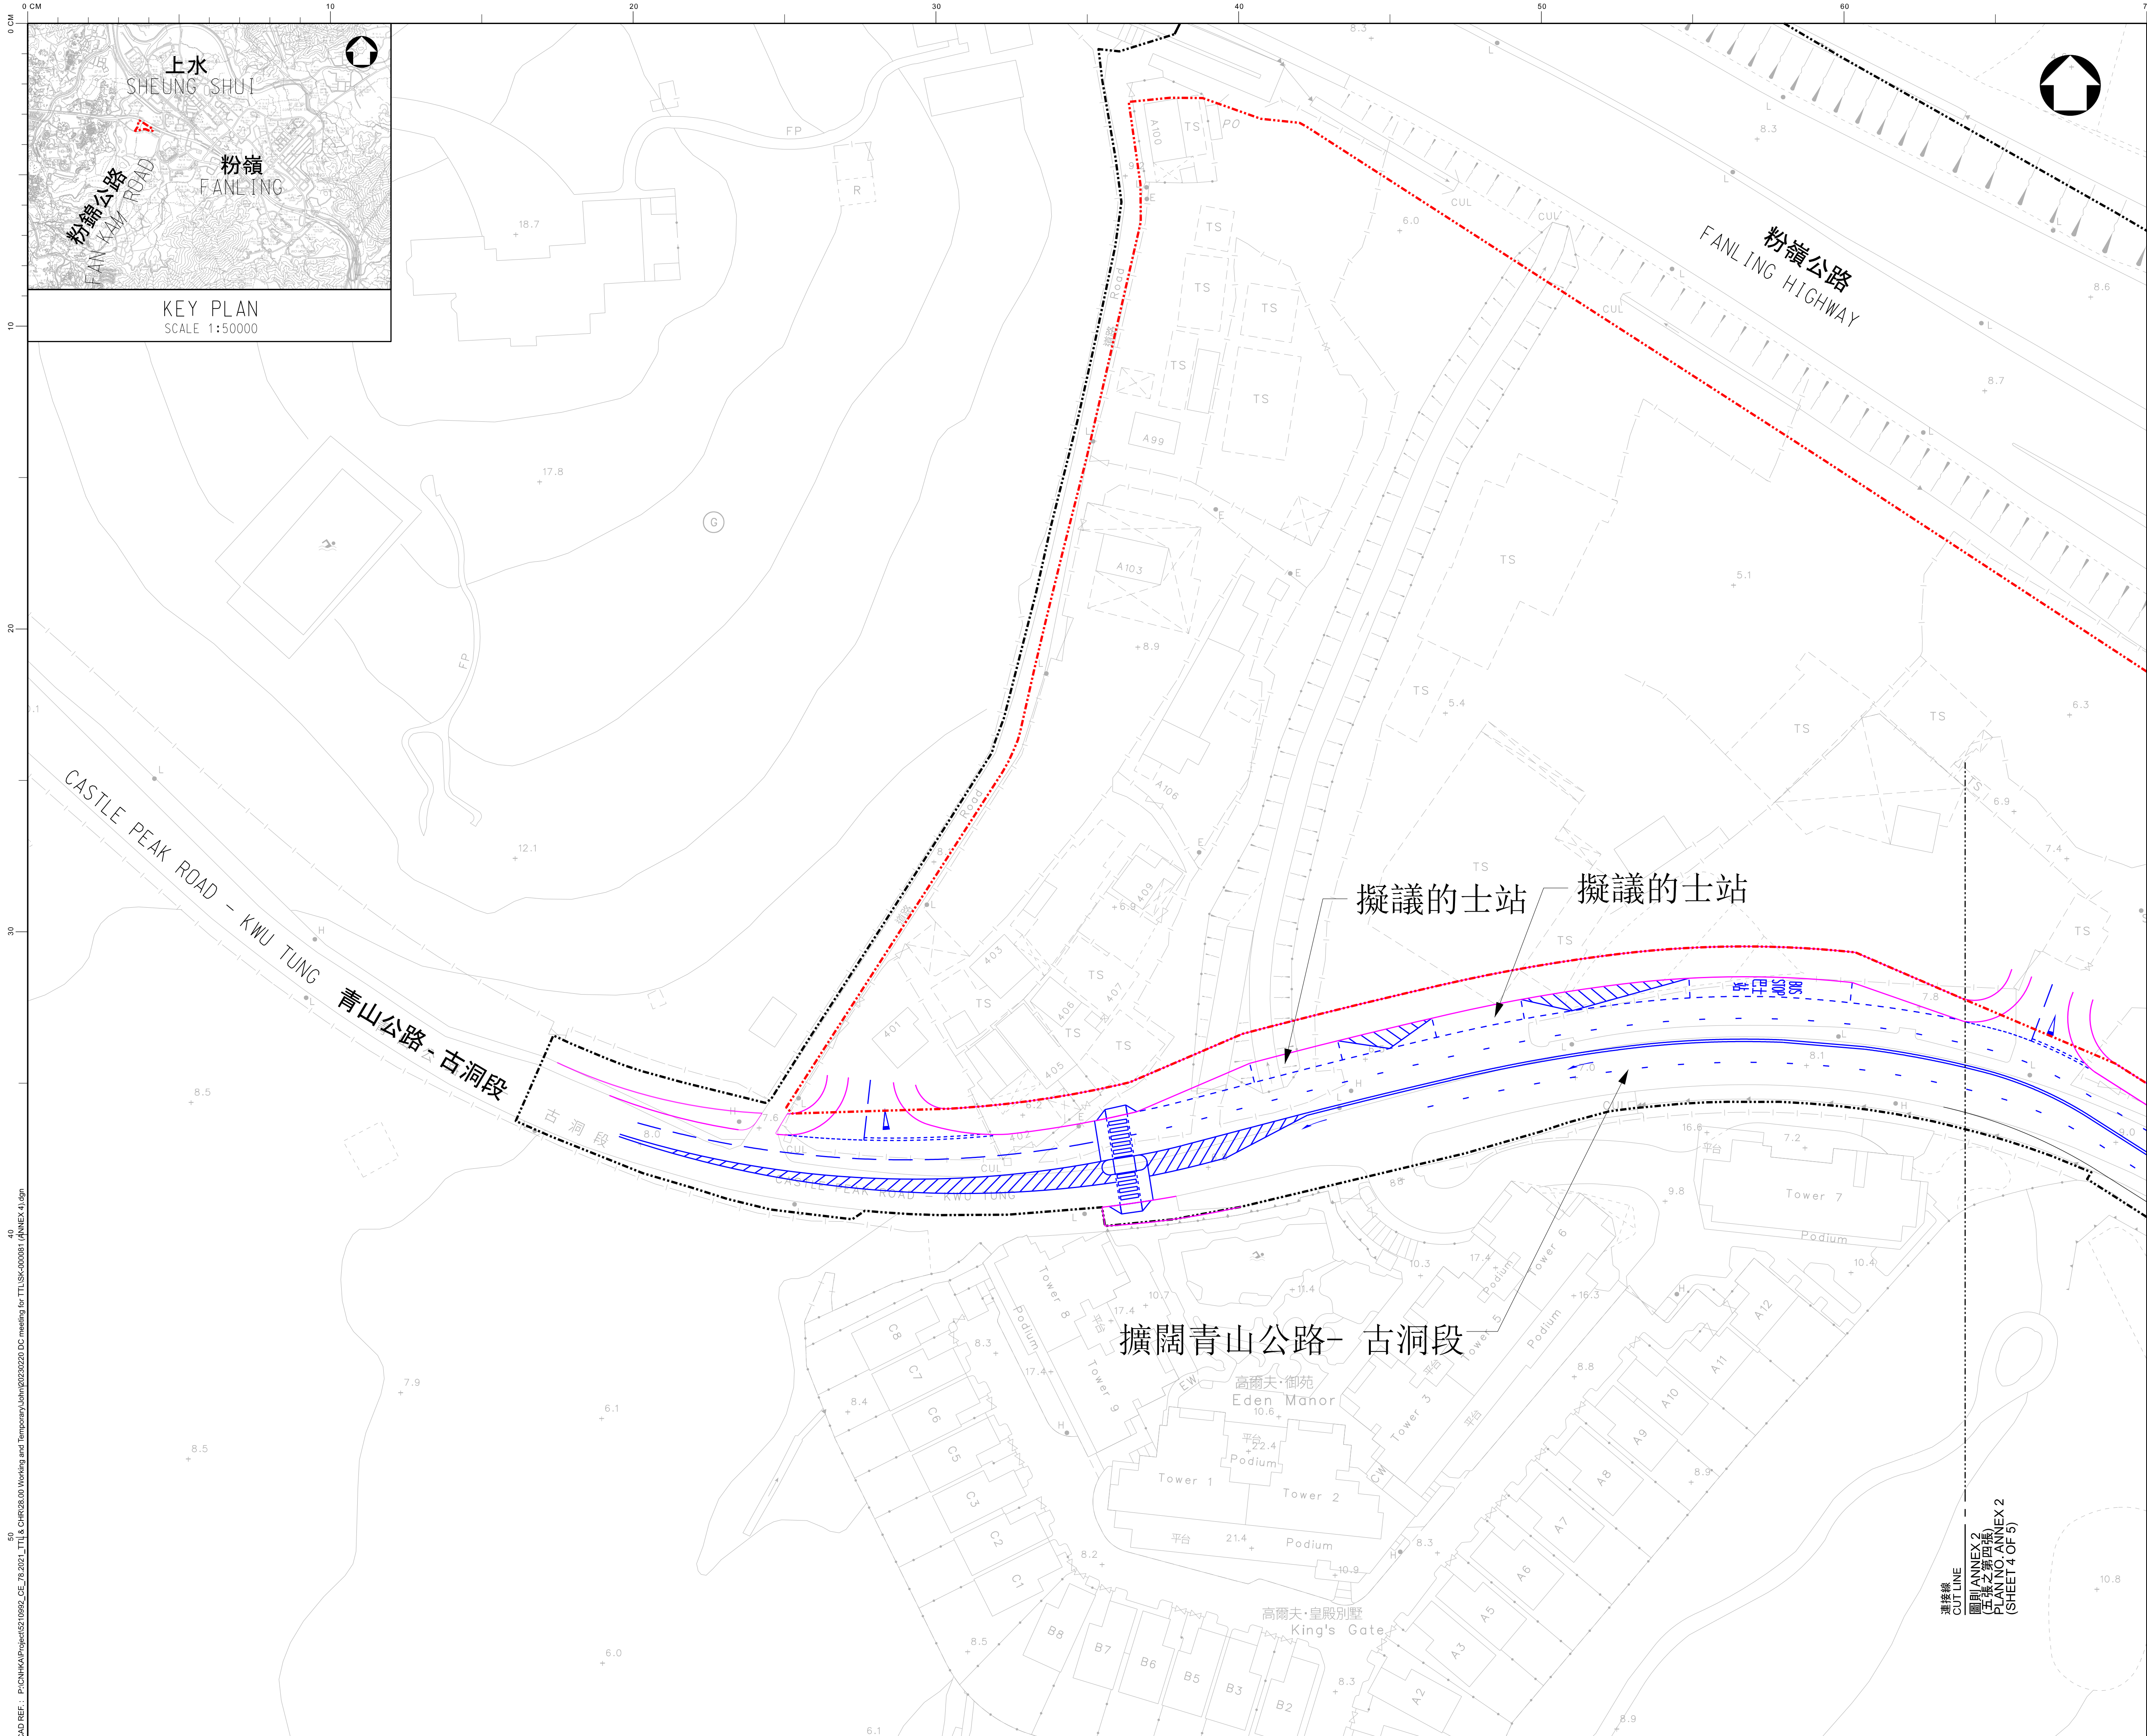

- 註釋 NOTES:
- 除特別註明外，全部以米為量度單位。
ALL DIMENSIONS ARE IN METERS UNLESS OTHERWISE STATED.
 - 所有水平均為約數以米為單位，並在香港主水平基準上。
ALL LEVELS ARE IN APPROXIMATE VALUES AND IN METRES ABOVE HONG KONG PRINCIPAL DATUM.
 - 如有需要，施工區界限內部分現有的停車灣、行車道、行人路及安全島或會分階段暫時封閉。
SECTIONS OF THE EXISTING LAY-BY, CARRIAGEWAYS, FOOTPATHS AND TRAFFIC ISLANDS WITHIN THE LIMIT OF WORKS AREA MAY BE TEMPORARILY CLOSED IN PHASES AS AND WHEN REQUIRED.

- 圖例 LEGEND:
- 擬議工地平整、排污、排水、供水、道路及路口改善工程施工區介限 (註釋3)
LIMIT OF WORKS AREA FOR PROPOSED SITE FORMATION, SEWERAGE, DRAINAGE, WATER SUPPLY, ROAD AND JUNCTION IMPROVEMENT WORKS (NOTE 3)
 - 擬議發展地盤
PROPOSED DEVELOPMENT SITE
 - 擬議路線
PROPOSED ROAD KERB
 - 擬議道路標記
PROPOSED ROAD MARKING

工程名稱 PROJECT TITLE
工務計劃項目第B869CL號
上水大頭嶺公共房屋發展
之地平整及基礎設施工程
PWP ITEM NO. B869CL
SITE FORMATION AND INFRASTRUCTURE
WORKS FOR PUBLIC HOUSING DEVELOPMENTS
AT TAI TAU LENG


圖則名稱 PLAN TITLE
擬議工地平整及基礎設施工程平面圖
(五張之第三張)
LAYOUT PLAN FOR SITE FORMATION
AND INFRASTRUCTURE WORKS
(SHEET 3 OF 5)

圖則編號 PLAN NO.
附錄二
ANNEX 2

部門 OFFICE
北拓展處
NORTH DEVELOPMENT OFFICE

 **土木工程拓展署**
Civil Engineering and
Development Department

CAD REF.: P:\CN\KAP\Project\210852_CE_12-2021_T11 & CHR28-01 Working and Temporary\Join\20220220 DC meeting for T11\SK-d00001 (ANNEX 4).dgn
40
50
CAD REF.: P:\CN\KAP\Project\210852_CE_12-2021_T11 & CHR28-01 Working and Temporary\Join\20220220 DC meeting for T11\SK-d00001 (ANNEX 4).dgn

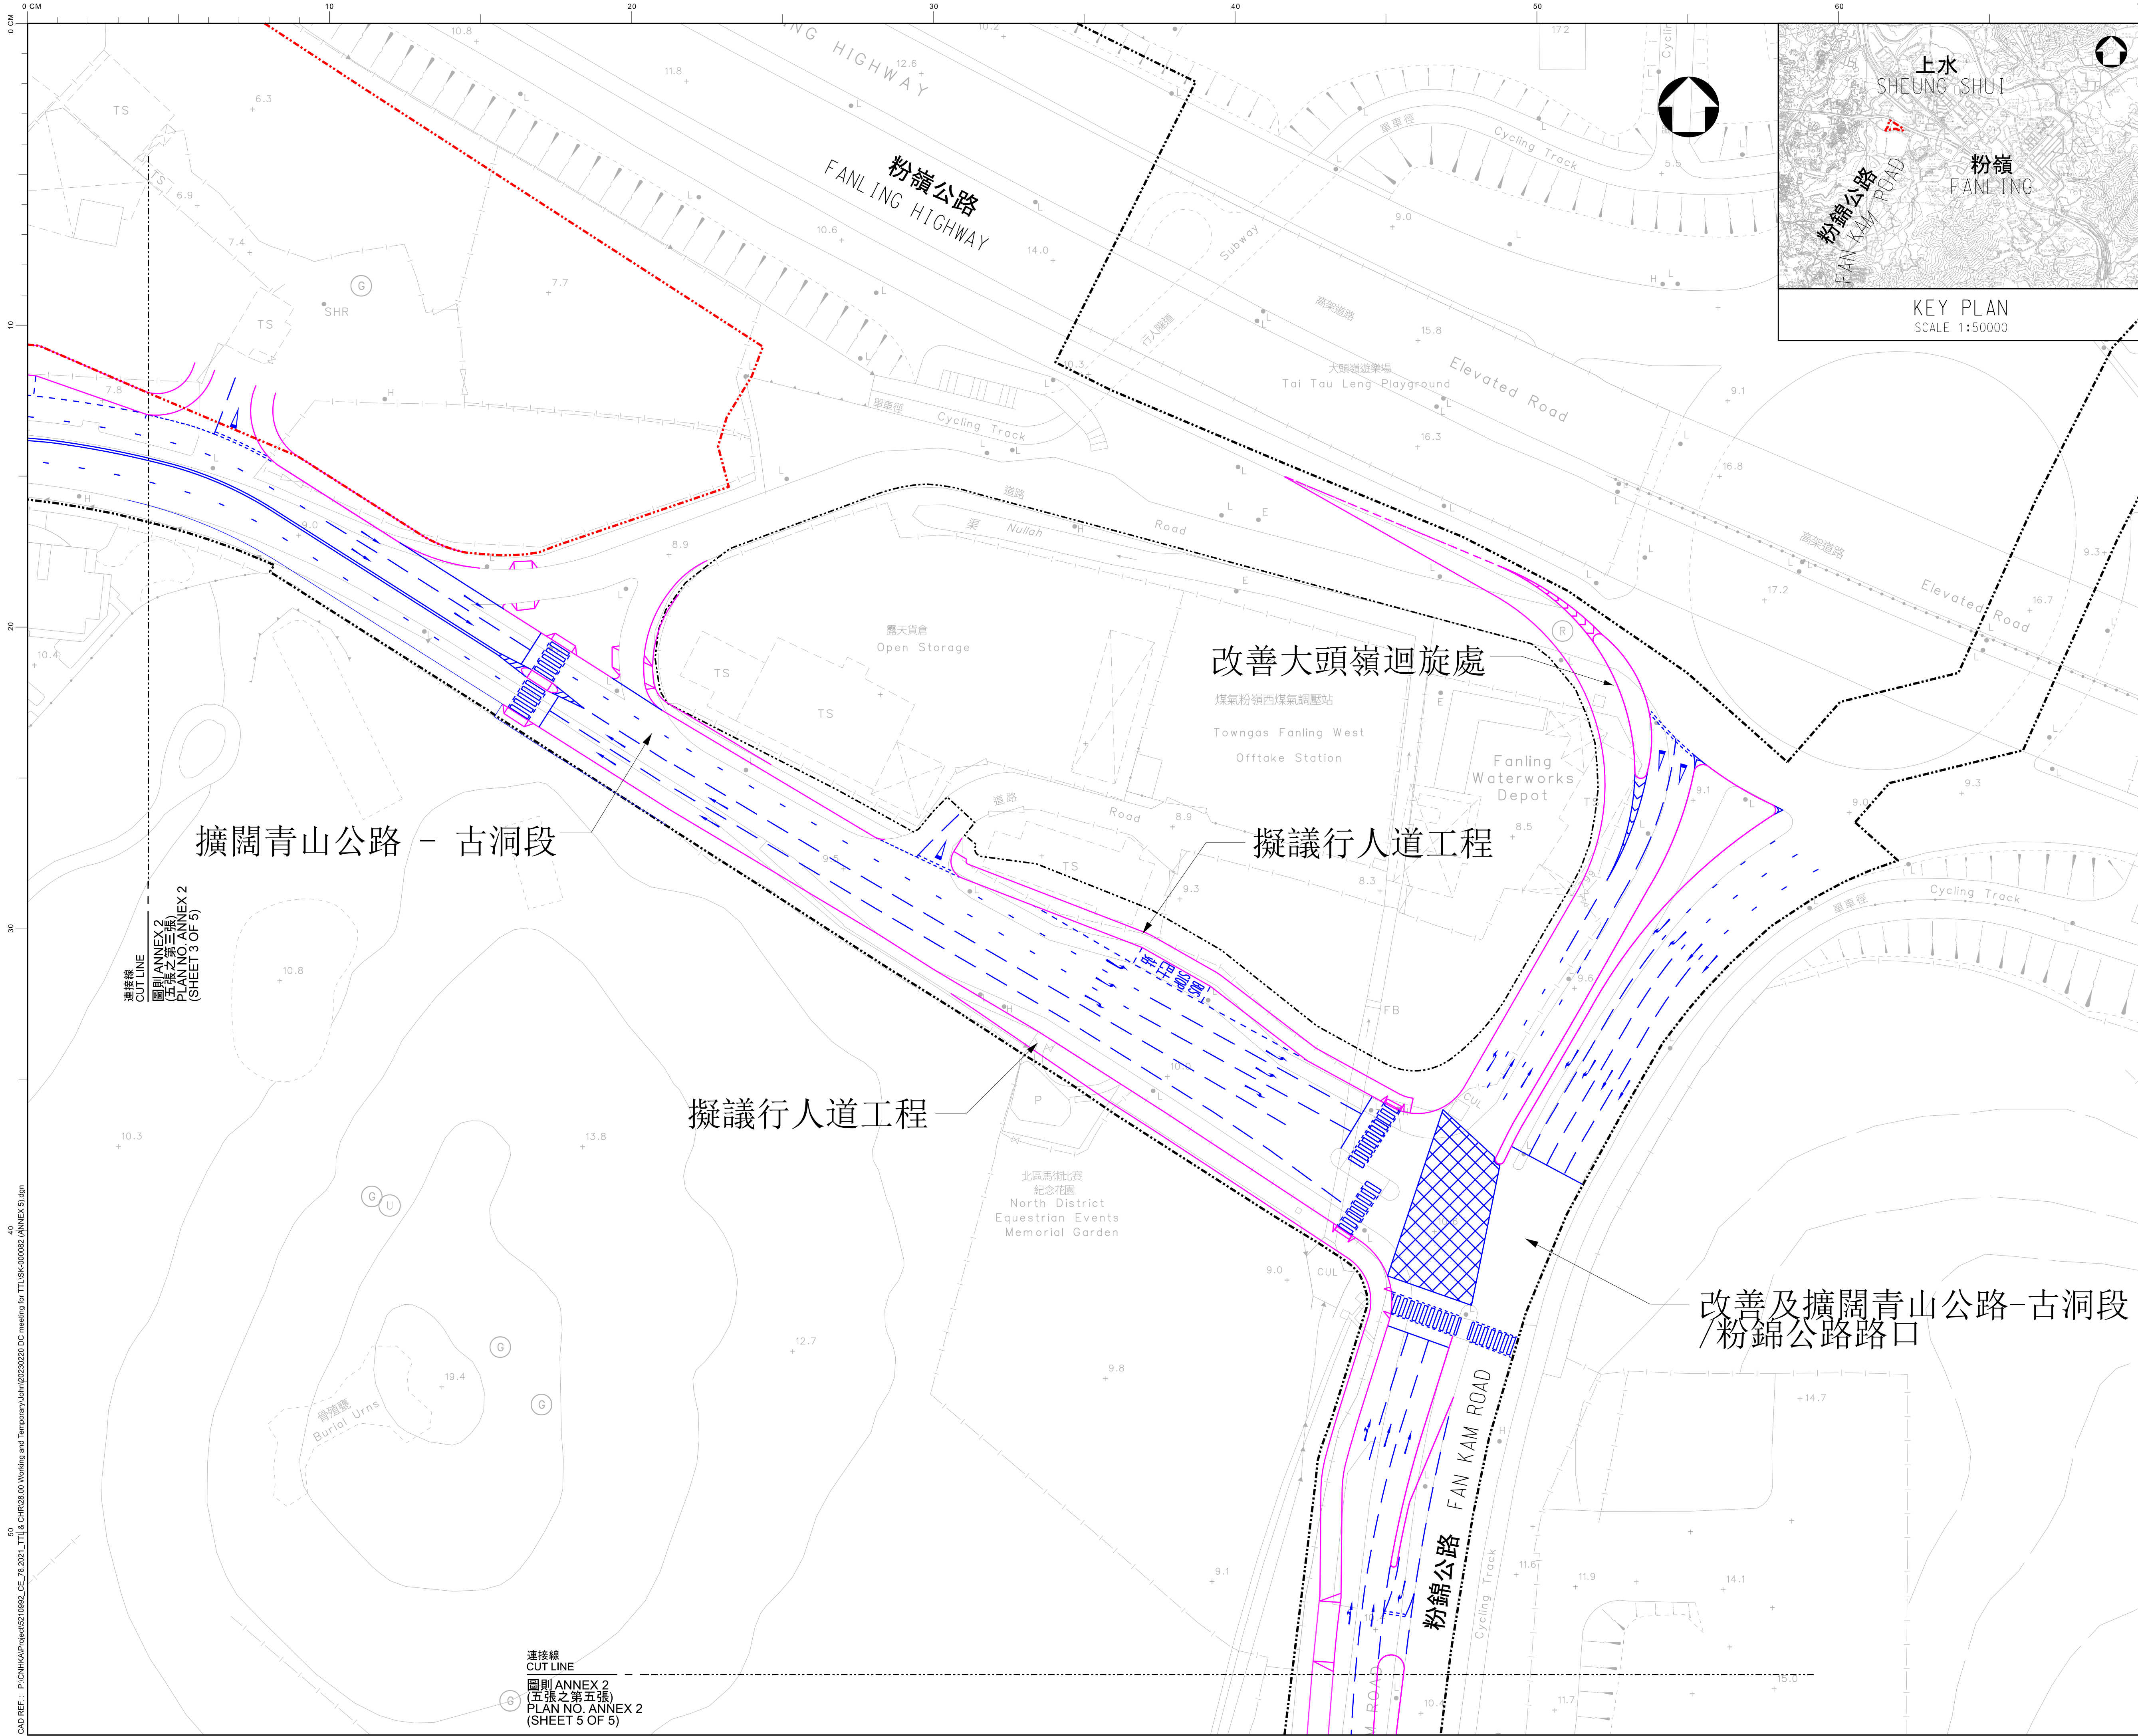

- 註釋 NOTES:
- 除特別註明外，全部以米為量度單位。
ALL DIMENSIONS ARE IN METERS UNLESS OTHERWISE STATED.
 - 所有水平均為約數以米為單位，並在香港主水平基準上。
ALL LEVELS ARE IN APPROXIMATE VALUES AND IN METRES ABOVE HONG KONG PRINCIPAL DATUM.
 - 如有需要，施工區界限內部分現有的停車灣、行車道、行人路及安全島或會分階段暫時封閉。
SECTIONS OF THE EXISTING LAY-BY, CARRIAGEWAYS, FOOTPATHS AND TRAFFIC ISLANDS WITHIN THE LIMIT OF WORKS AREA MAY BE TEMPORARILY CLOSED IN PHASES AS AND WHEN REQUIRED.

- 圖例 LEGEND:
- 擬議工地平整、排污、排水、供水、道路及路口改善工程施工區介限 (註釋3)
LIMIT OF WORKS AREA FOR PROPOSED SITE FORMATION, SEWERAGE, DRAINAGE, WATER SUPPLY, ROAD AND JUNCTION IMPROVEMENT WORKS (NOTE 3)
 - 擬議發展地盤
PROPOSED DEVELOPMENT SITE
 - 擬議路線
PROPOSED ROAD KERB
 - 擬議道路標記
PROPOSED ROAD MARKING

工程名稱 PROJECT TITLE
工務計劃項目第B869CL號
上水大頭嶺公共房屋發展
之工地平整及基礎設施工程
PWP ITEM NO. B869CL
SITE FORMATION AND INFRASTRUCTURE
WORKS FOR PUBLIC HOUSING DEVELOPMENTS
AT TAI TAU LENG

圖則名稱 PLAN TITLE
擬議工地平整及基礎設施工程平面圖
(五張之第四張)
LAYOUT PLAN FOR SITE FORMATION
AND INFRASTRUCTURE WORKS
(SHEET 4 OF 5)

圖則編號 PLAN NO.
附錄二
ANNEX 2

比例 SCALE
1:500

部門 OFFICE
北拓展處
NORTH DEVELOPMENT OFFICE

CEDD 土木工程拓展署
Civil Engineering and
Development Department

